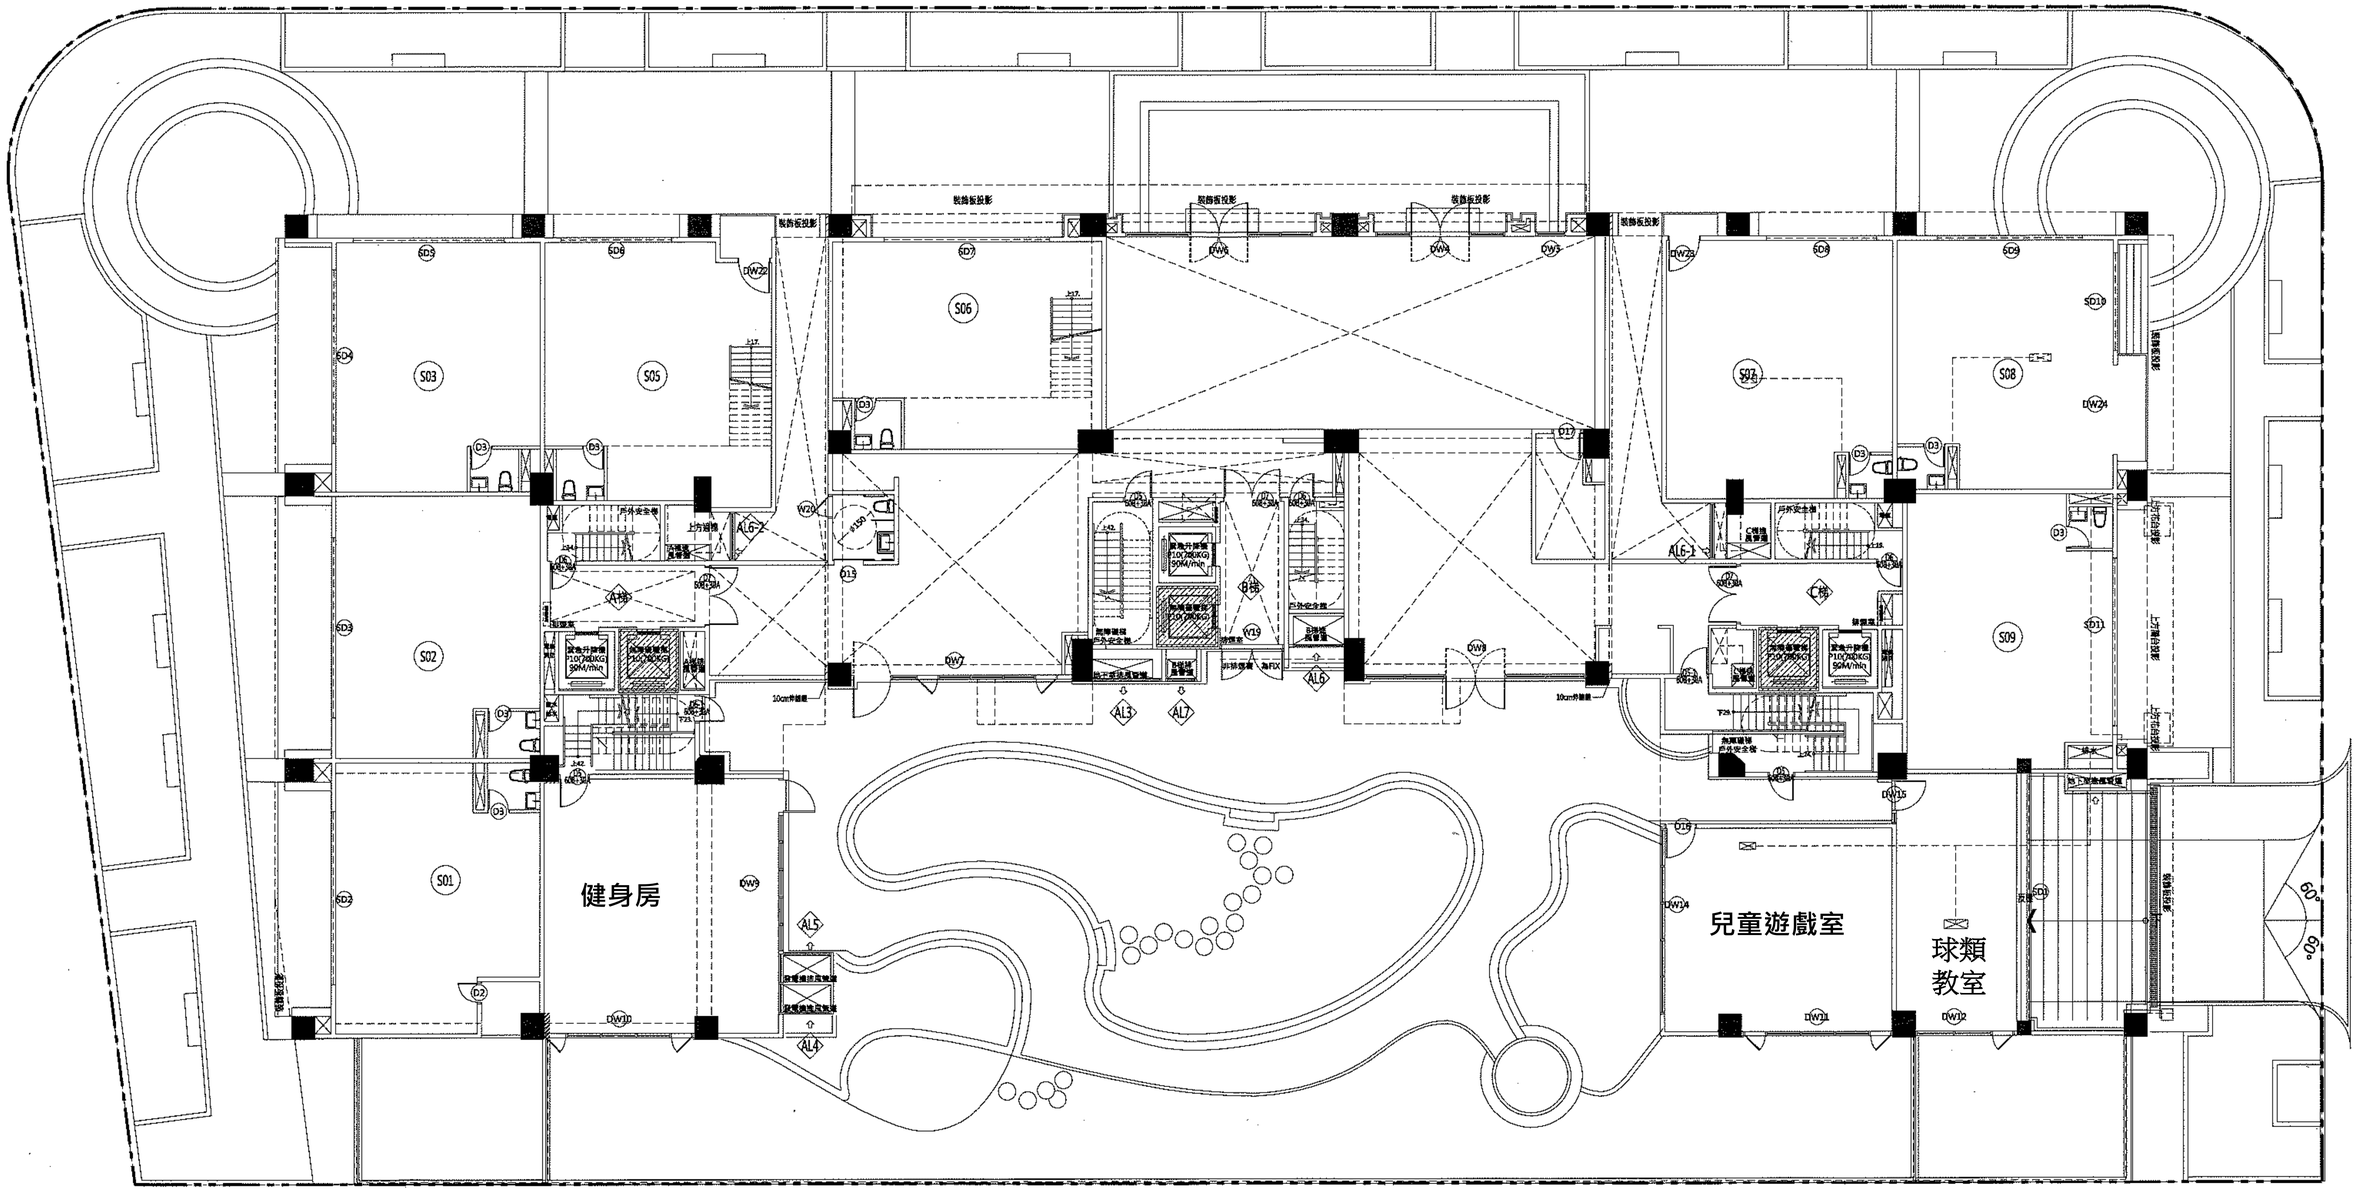
S01
S02
S03
S05
S06
S07
S08
S09
健身房
兒童遊戲室
球類
教室
裝飾板投影
戶外安全梯
上方通道
AL6-2
AL6-1
AL3
AL7
AL6
AL5
AL4
A-BB
B-BB
C-BB
60°
60°

1F

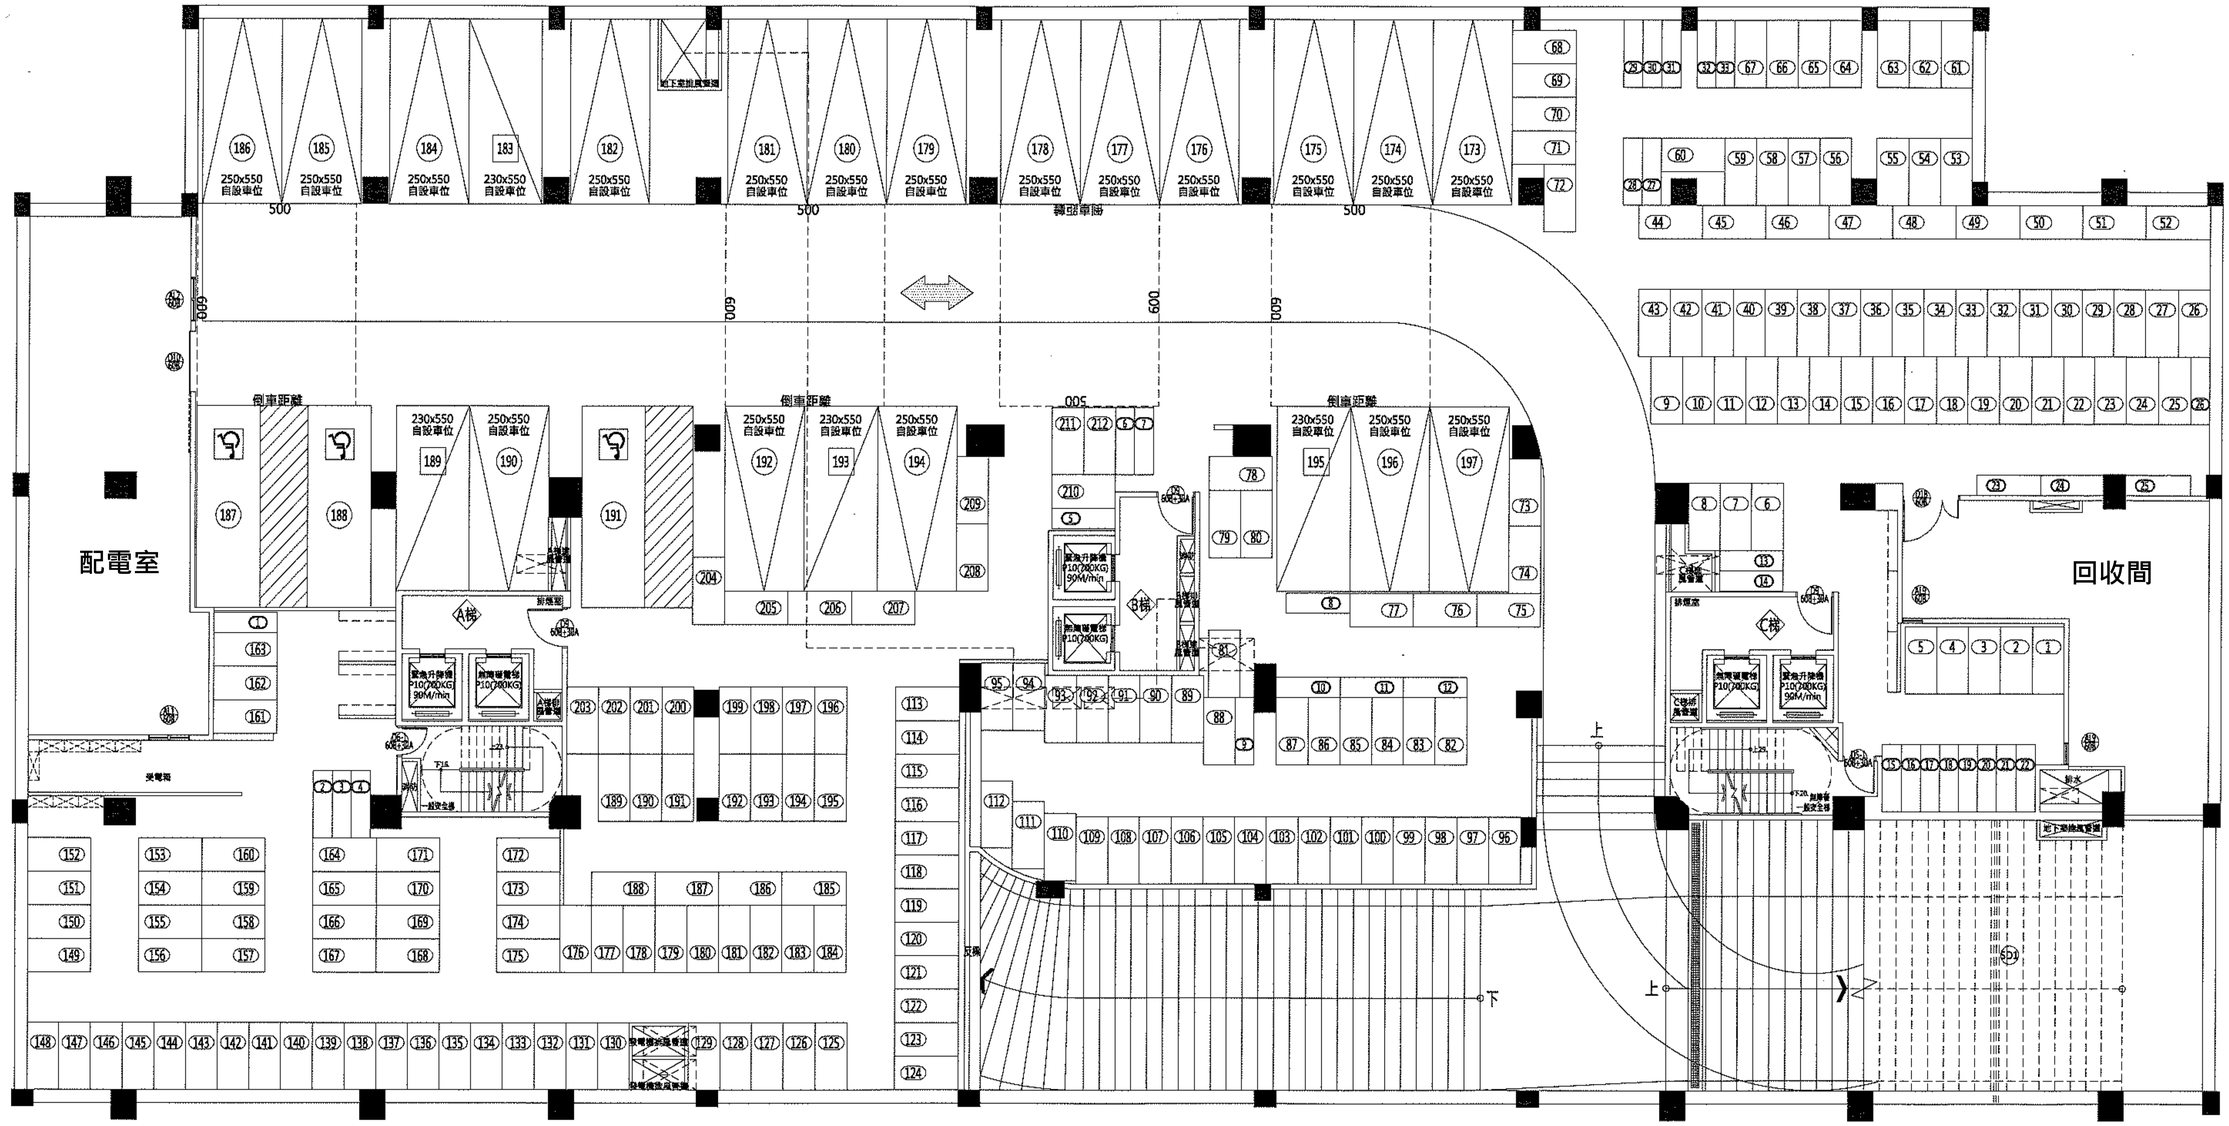
配電室
回收間
250x550
自設車位
230x550
自設車位
轉彎車輛
倒車距離
500
600
A梯
B梯
C梯
緊急升降機
P10(200KG)
90M/min
消防電梯
P10(200KG)
C梯消防
排煙室
一般安全梯
下
上

B1F

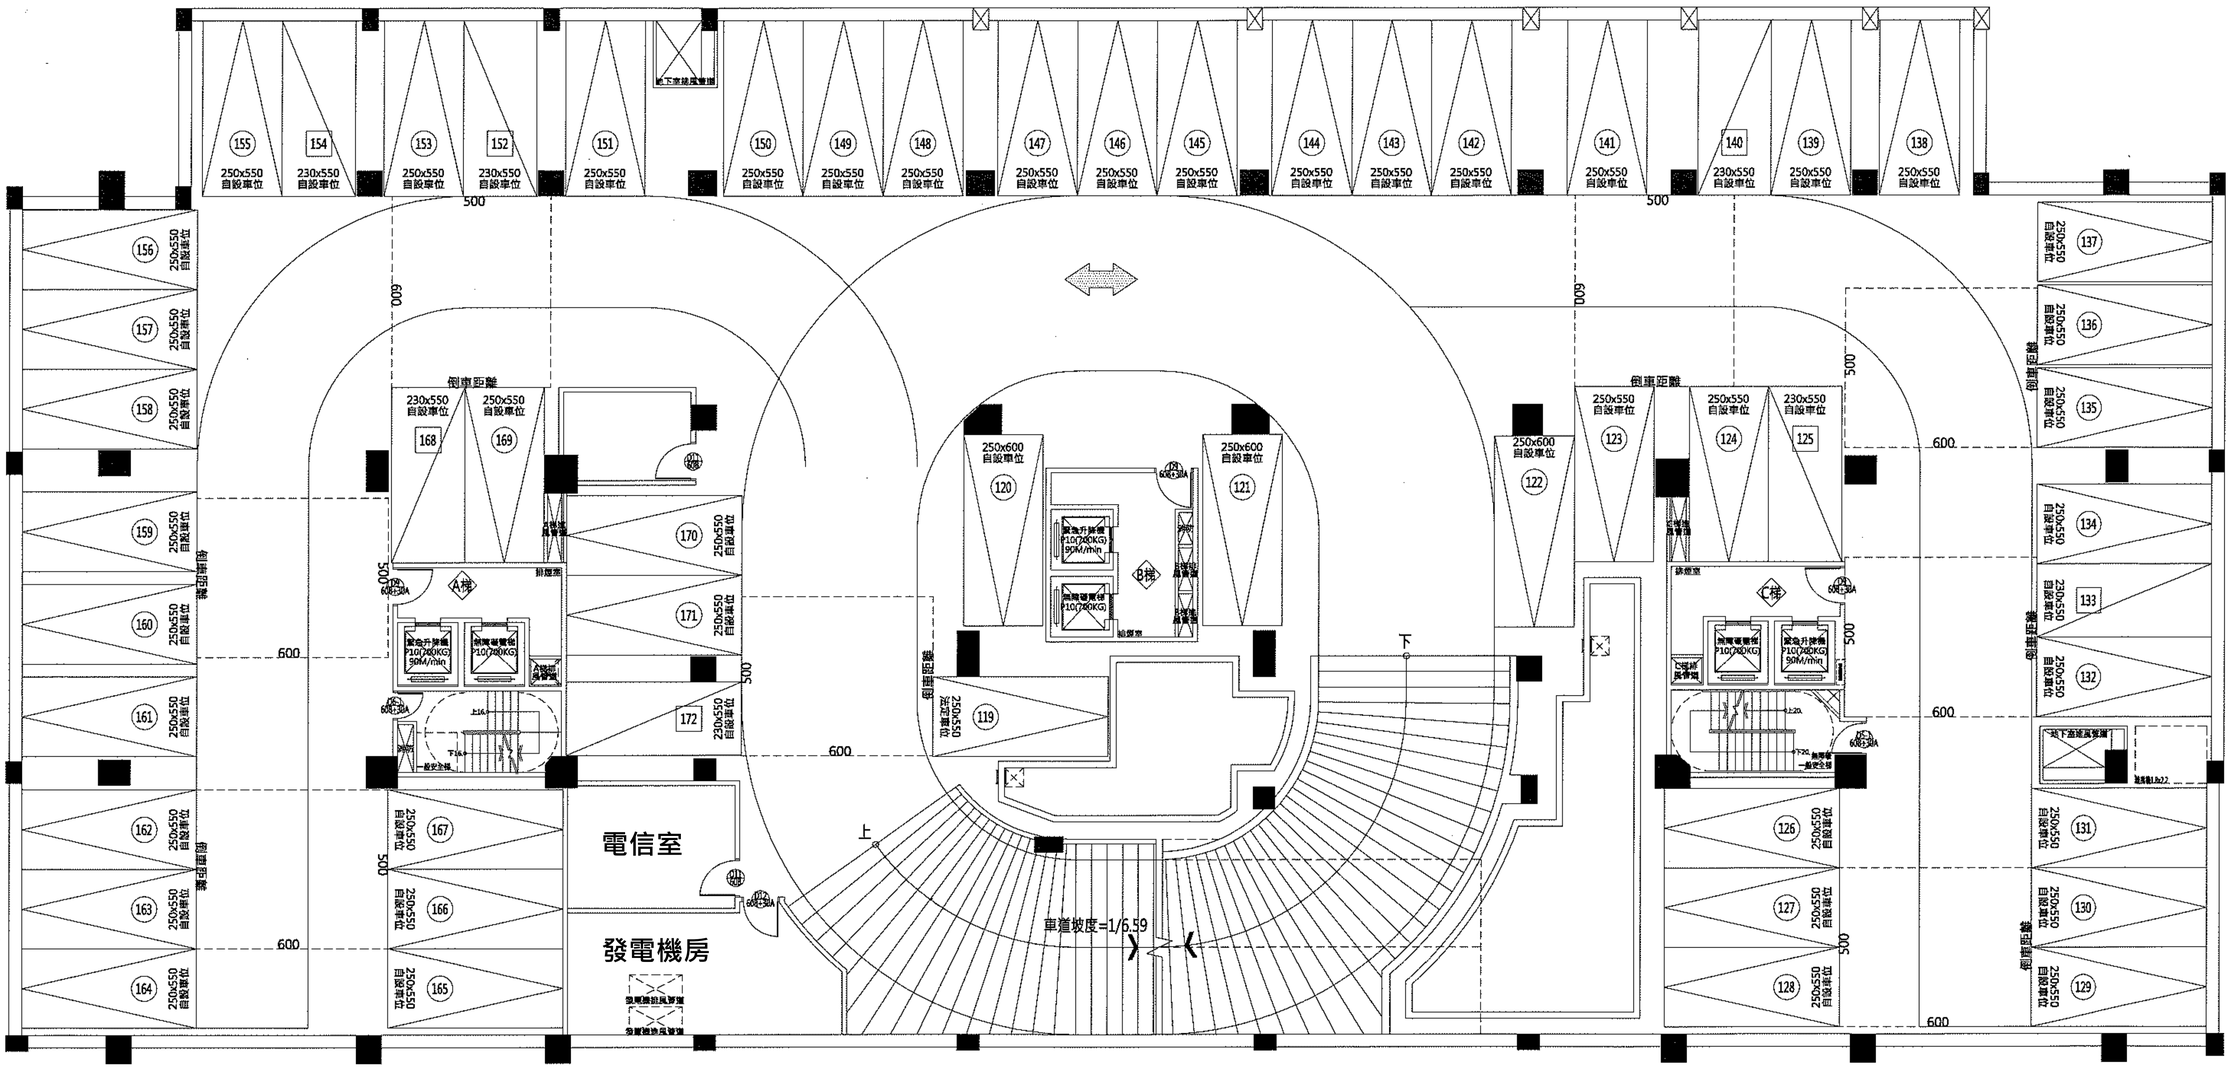
電信室
發電機房
車道坡度=1/6.59
A梯
B梯
C梯
緊急升降機 P10(700KG) 90M/min
緊急升降機 P10(700KG) 50M/min
消防電梯 P10(700KG)
排煙室
倒車距離
250x550 自設車位
230x550 自設車位
250x600 自設車位
600
500

B2F

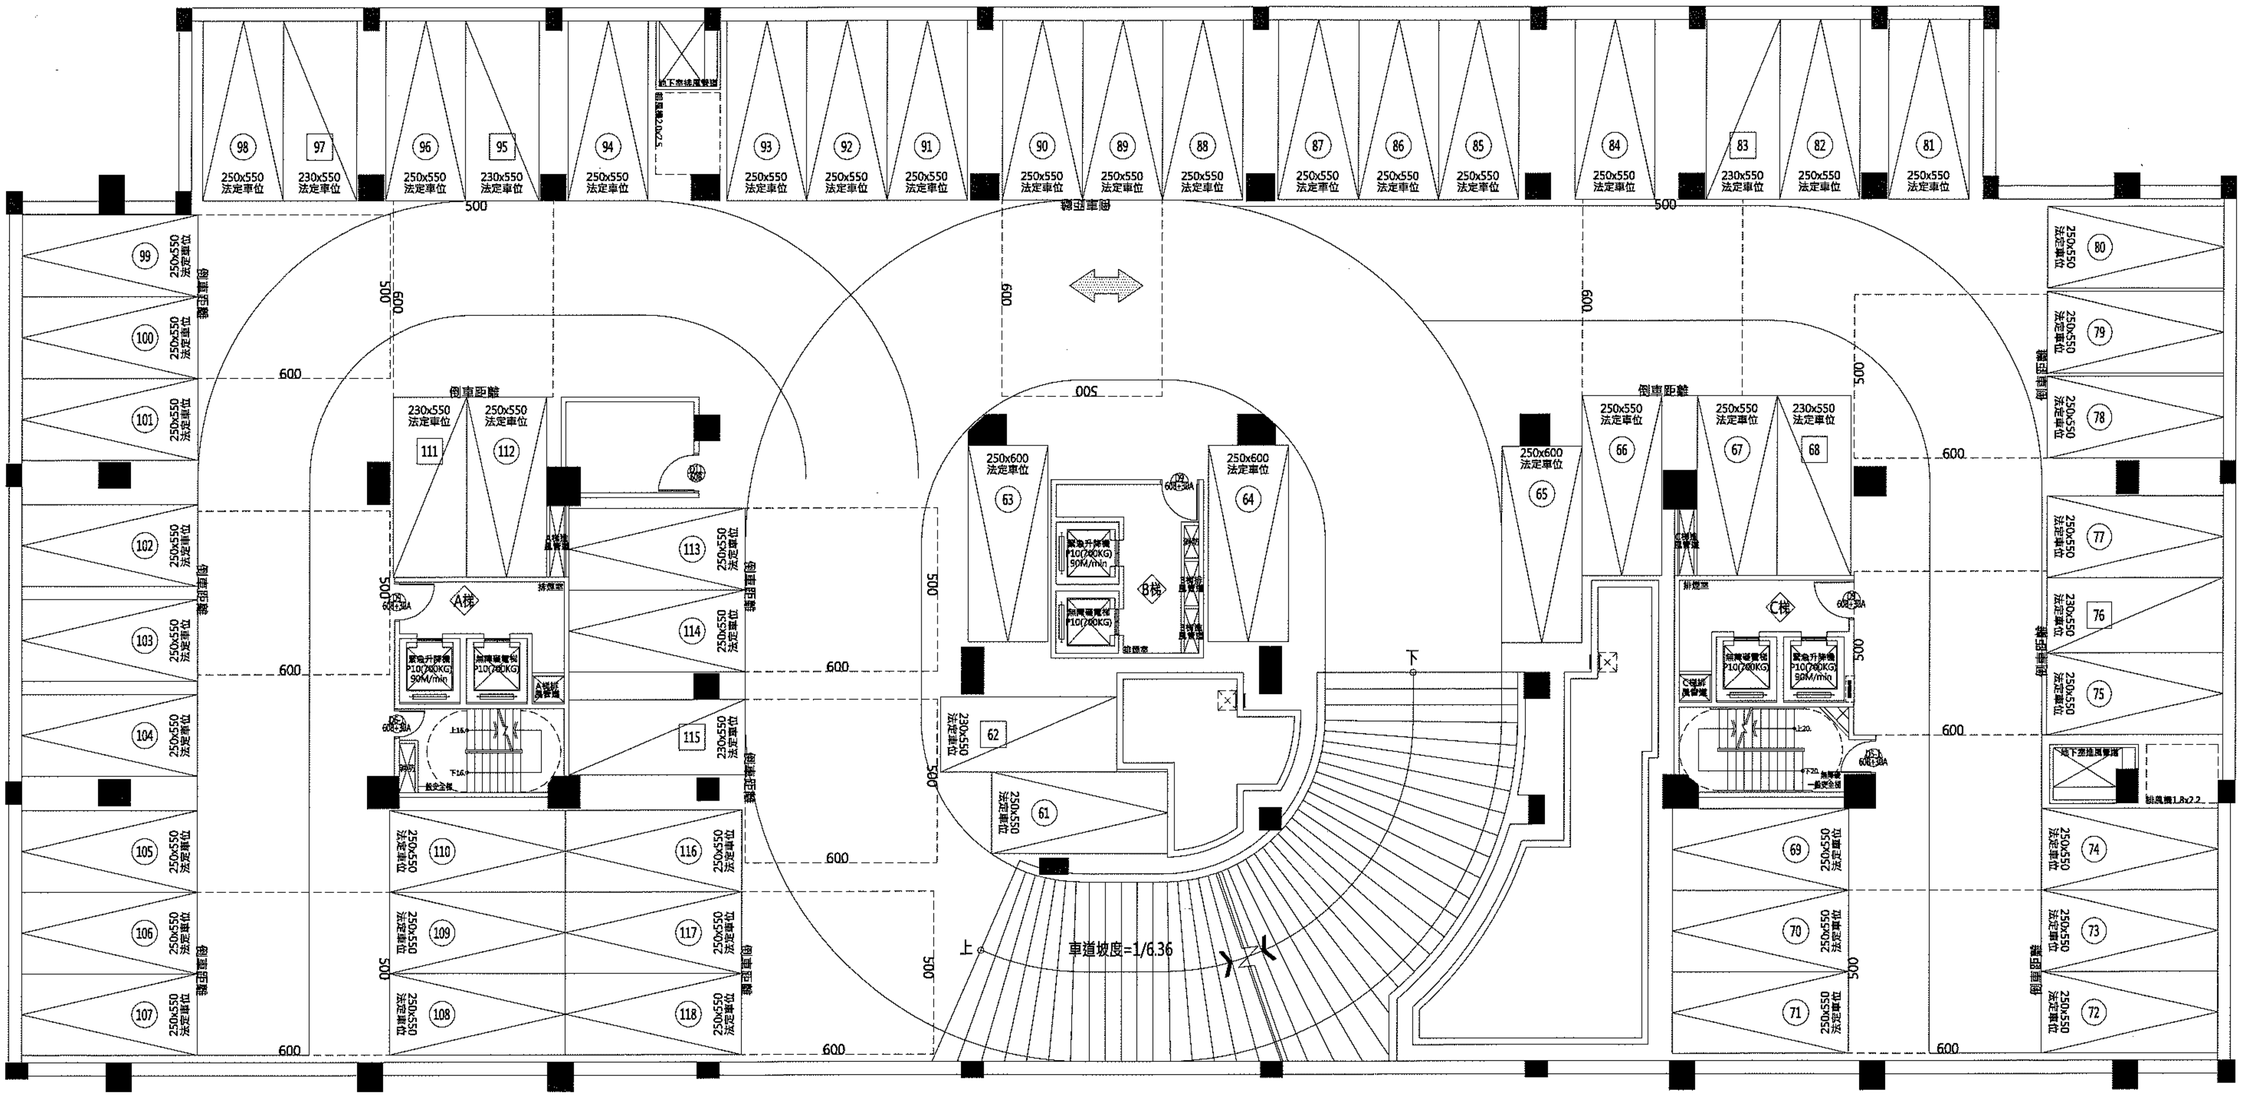
250x550 法定車位
230x550 法定車位
250x600 法定車位
倒車距離
車道坡度=1/6.36
A梯
B梯
C梯
緊急升降機 P10(700KG) 90M/min
加壓排煙機 P10(700KG)
排煙室
消防栓箱
滅火器
一般安全板
上16
下16
上20
下20
60E30A
鋁風機1.8x2.2
給下水排風管道
500
600

B3F

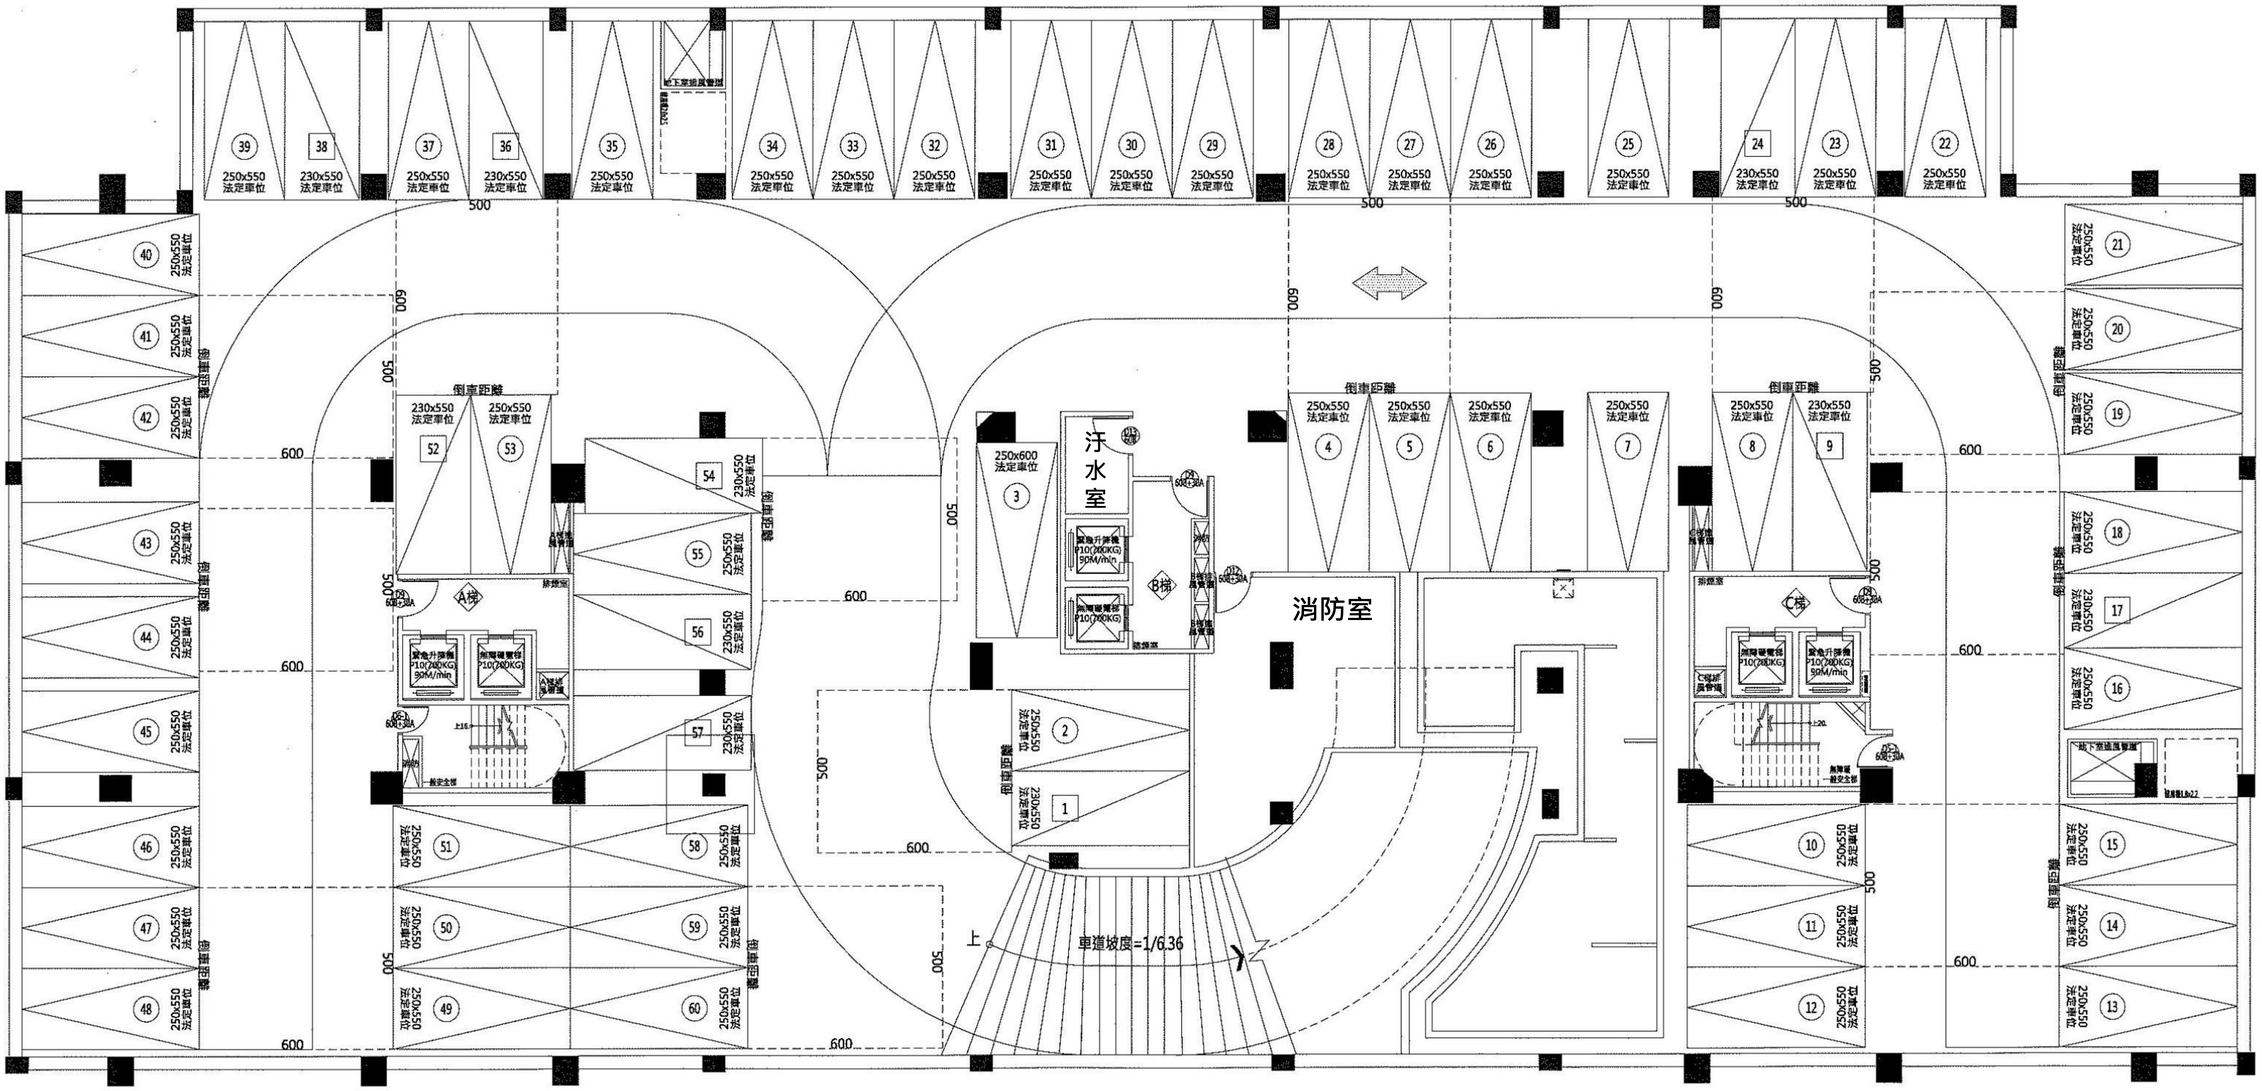
消防室
汚水室
車道坡度=1/6.36
倒車距離
A梯
B梯
C梯
250x550 法定車位
230x550 法定車位
250x600 法定車位

B4F